


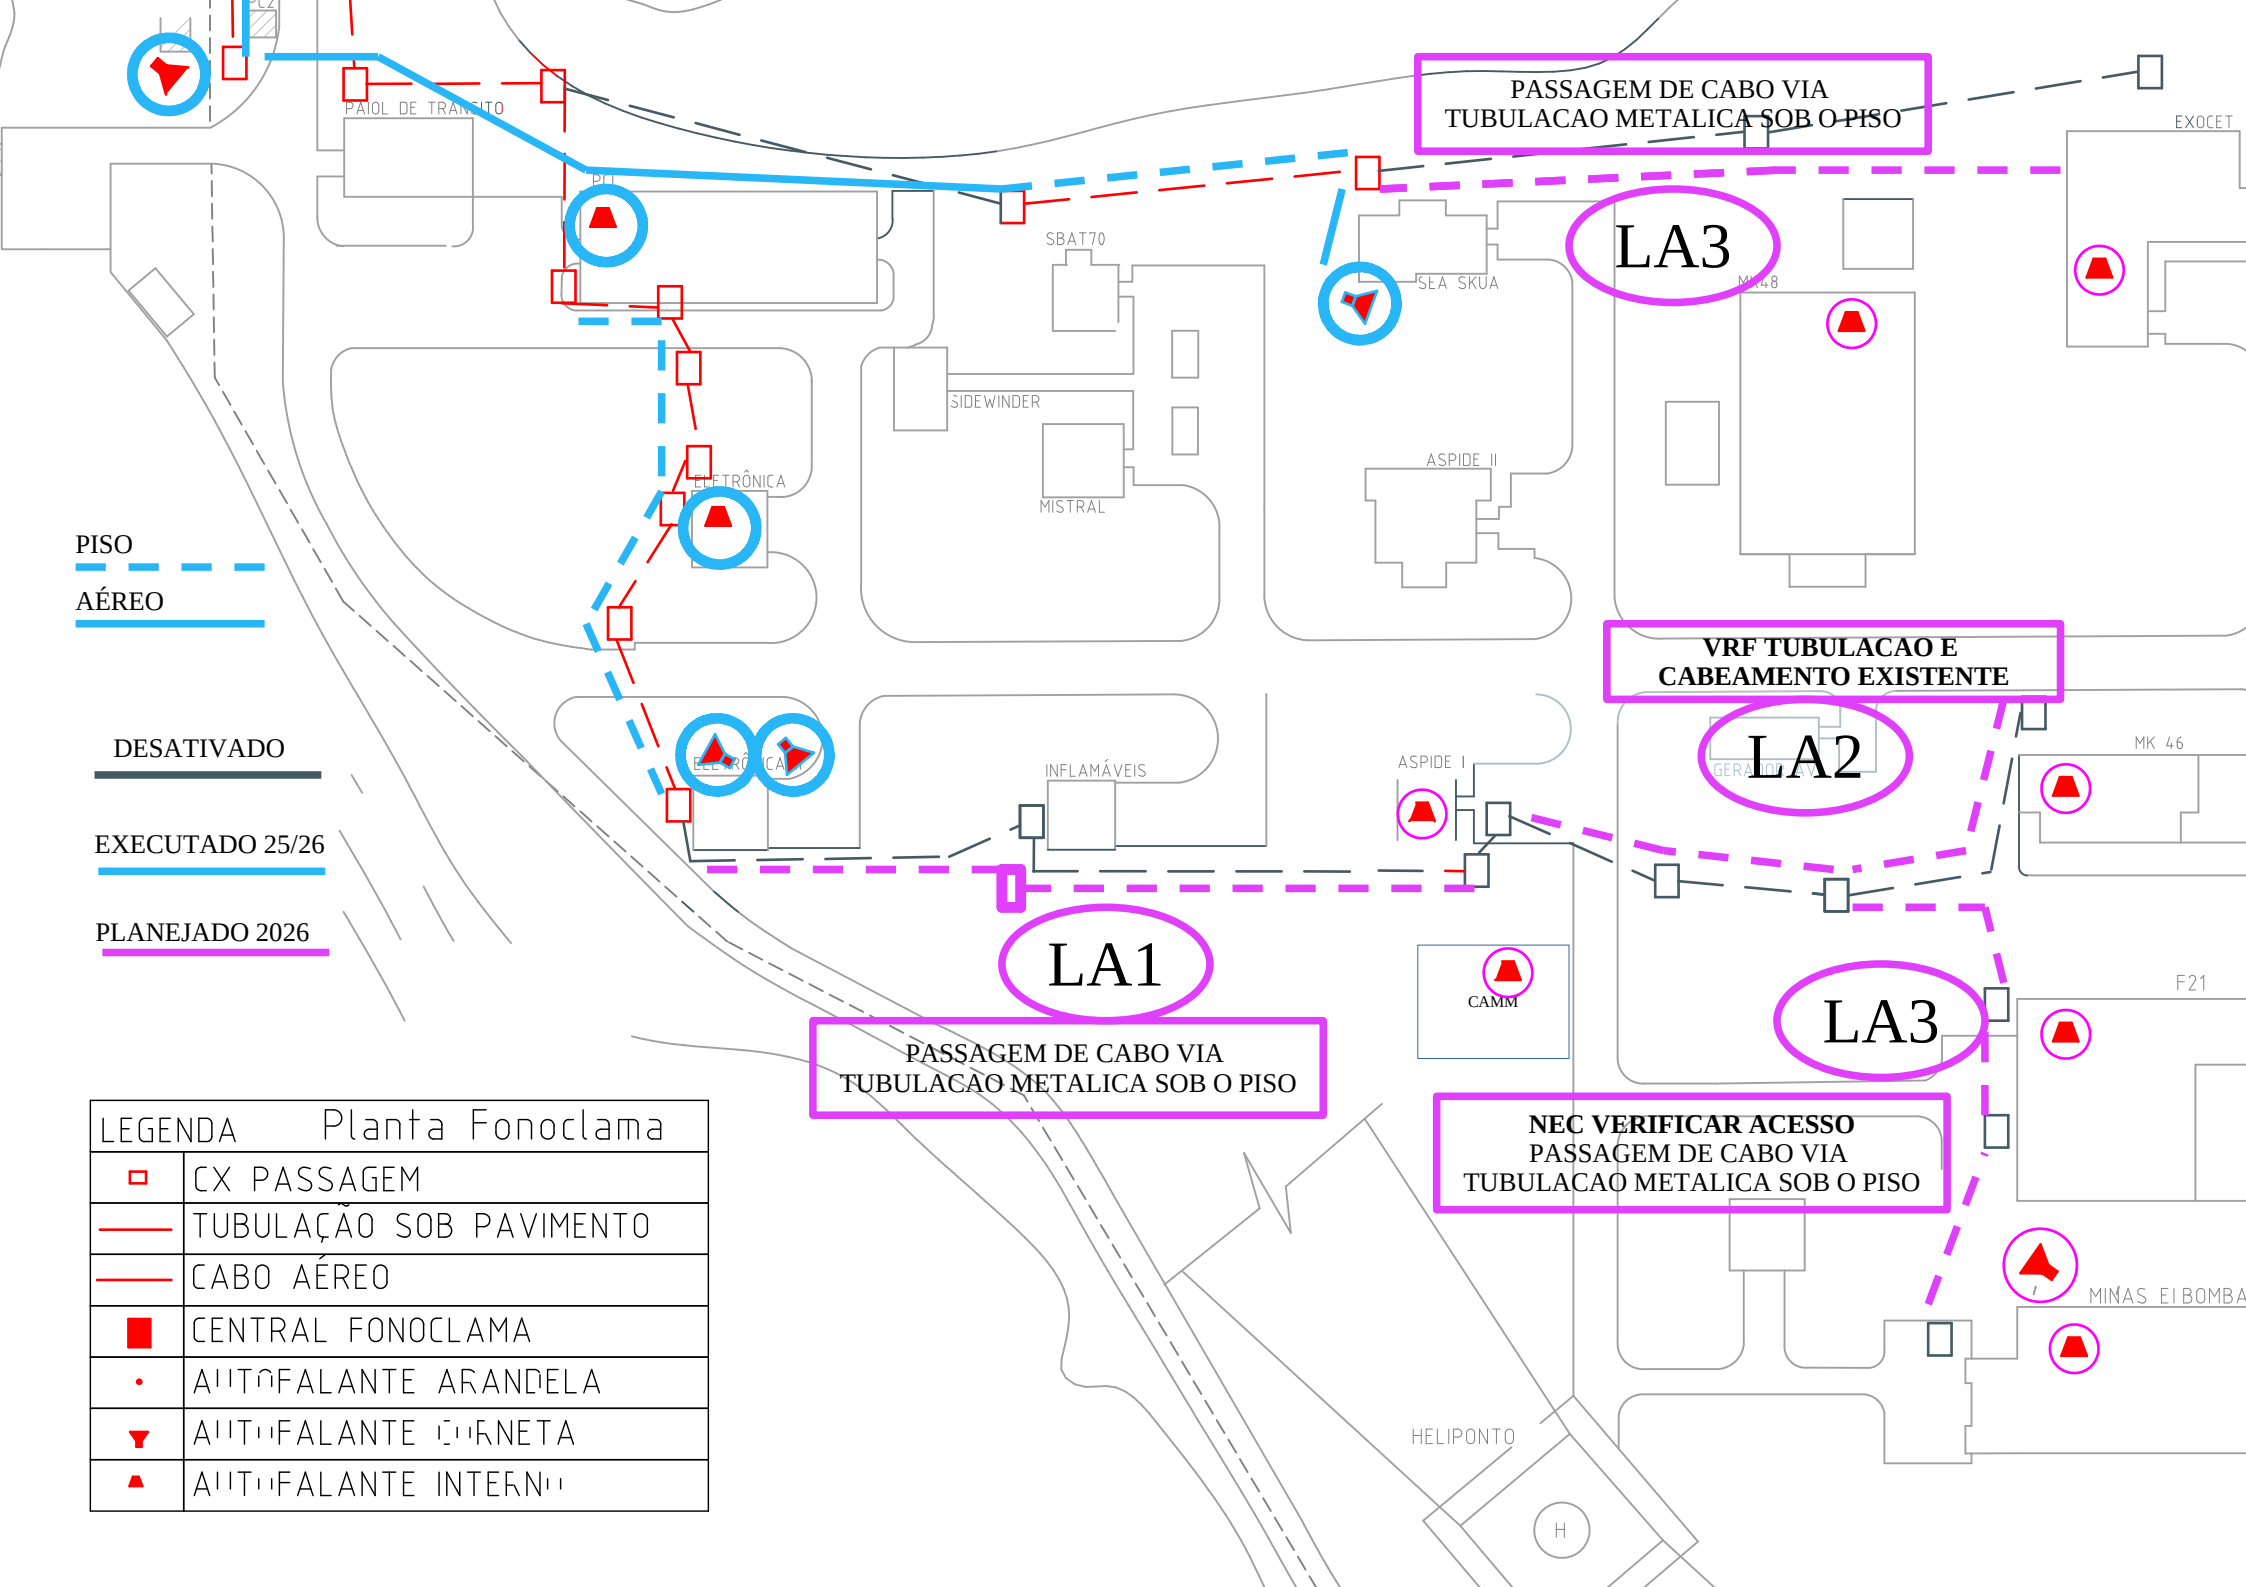

PISO
AÉREO

DESATIVADO

EXECUTADO 25/26

PLANEJADO 2026

LEGENDA Planta Fonoclama	
	CX PASSAGEM
	TUBULAÇÃO SOB PAVIMENTO
	CABO AÉREO
	CENTRAL FONOCLAMA
	ALTOFALANTE ARANDELA
	ALTOFALANTE CILÍNDRICA
	ALTOFALANTE INTERNO